
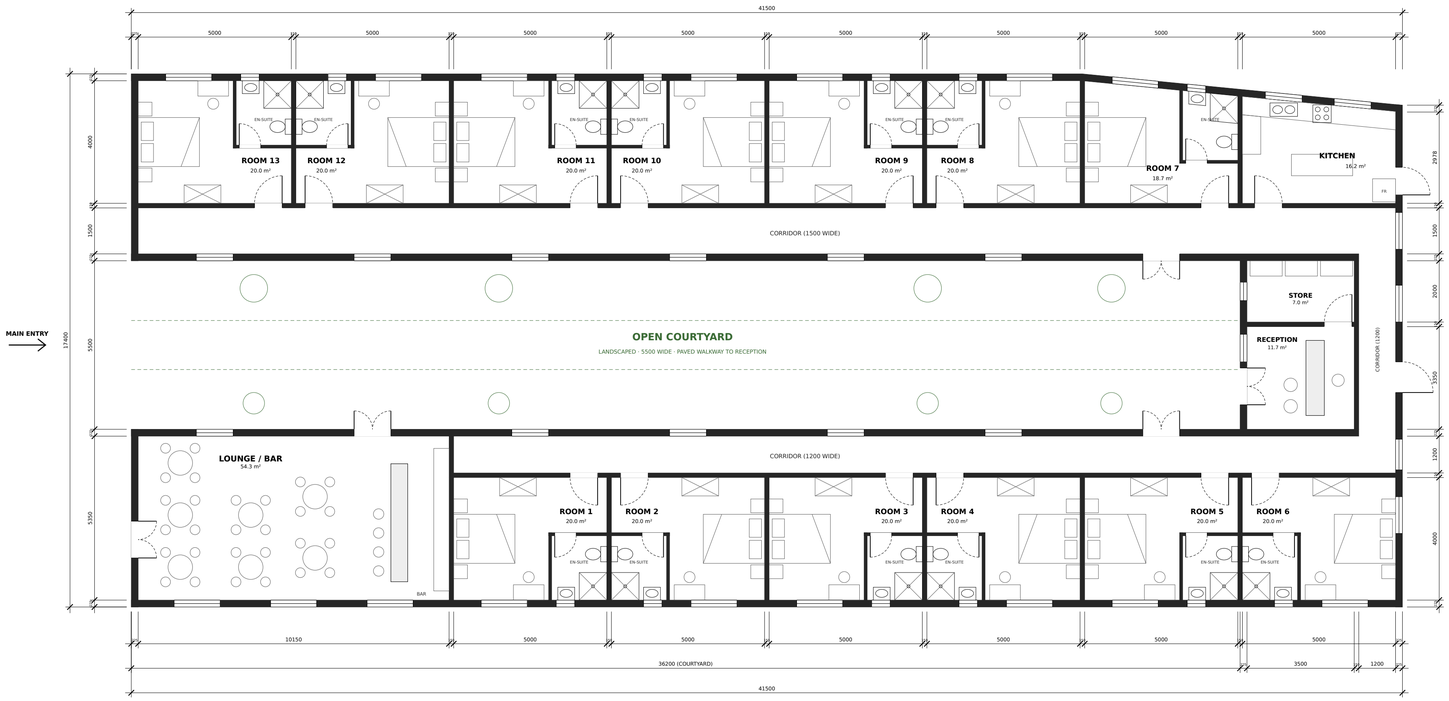


GROUND FLOOR PLAN

SCALE 1:100 @ A1 · ALL DIMENSIONS IN MILLIMETRES

SCALE 1:100 (METRES)

0 1 2 3 4 5

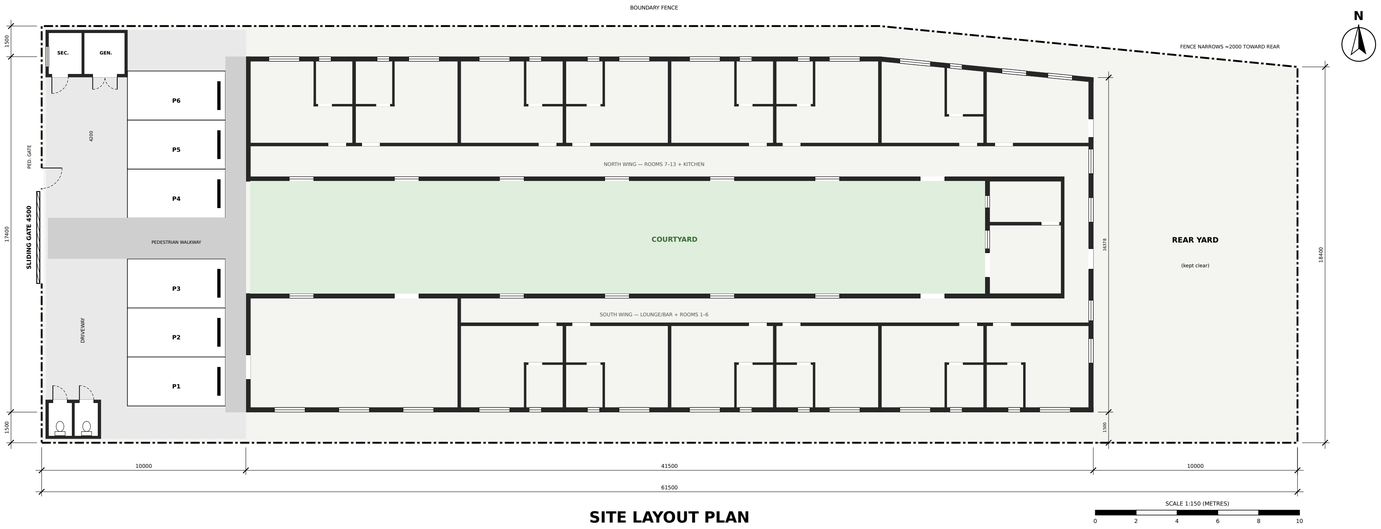

SITE LAYOUT PLAN

SCALE 1:150 @ A1 · SETBACKS: FRONT 10 m · REAR 10 m · SIDES 1.5 m

SCALE 1:150 (METRES)

0 2 4 6 8 10

N

(ASSUMED)

LEGEND

- 225 mm sandcrete block wall (external)
- 150 mm block wall (internal partition)
- 100 mm block wall (en-suite partition)
- Door (leaf + swing)
- Window
- WC · wash-hand basin · shower tray
- Dimension (mm)
- Boundary fence

DOOR & WINDOW SCHEDULE

MARK	SIZE (mm)	TYPE	LOCATION
D1	1200 × 2100	Double-leaf, glazed/panel	Corridor↔courtyard, lounge↔courtyard, reception; lounge front
D2	1000 × 2100	Single-leaf, solid	Rear corridor exit
D3	900 × 2100	Single-leaf flush + louvred fanlight	Guest rooms, kitchen, store
D4	700 × 2100	Single-leaf flush (PVC/WPC)	En-suite toilets
W1	1500 × 1200	Casement, sill 900, burglar-proof	Guest rooms, lounge
W2	1200 × 1200	Casement, sill 900, burglar-proof	Corridors (courtyard side), kitchen, reception
W3	600 × 600	High-level louvre, sill 1800	En-suite toilets, store

ACCOMMODATION SCHEDULE

SPACE	NO.	CLEAR SIZE (mm)	AREA m²
Guest rooms 1–6, 8–13 (en-suite)	12	5000 × 4000	20.0 each
Guest room 7 (slanted rear wall)	1	5000 × 3500–4000	18.7
En-suite toilet (WC, basin, shower)	13	1800 × 2100	3.8 each
Lounge / bar (no corridor)	1	10150 × 5350	54.3
Kitchen	1	5000 × 3000–3500	16.2
Reception	1	3500 × 3350	11.7
Store	1	3500 × 2000	7.0
Corridors: north / south / rear	3	1500 / 1200 / 1200 wide	—
Security post · generator room	1+1	1800 × 2200 · 1950 × 2200	4.0 · 4.3
Outdoor convenience (2 WCs)	1	2 × 1125 × 1600	3.6
Car parking bays	6	2400 × 4800	—
GROSS FLOOR AREA (main building)			**≈ 518**
Open courtyard		36200 × 5500	≈ 199
Plot (approx.)		61500 × 20400 / 18400	≈ 1234

Total guest rooms: 13 (all en-suite)

GENERAL NOTES

1. All dimensions are in millimetres unless otherwise stated. Do not scale from this drawing; use figured dimensions only.
2. Room sizes are clear internal dimensions (face of block to face of block), excluding plaster.
3. External walls: 225 mm (9") sandcrete hollow block. Internal partitions: 150 mm (6"). En-suite partitions: 100 mm (4").
4. Site setbacks: front (gate side) 10.0 m, rear 10.0 m, sides 1.5 m. Plot size derived from setbacks; confirm by survey plan.
5. North boundary narrows approx. 2.0 m toward the rear; Room 7 and kitchen outer wall follows the fence line, keeping 1.5 m clear.
6. North orientation assumed (top of sheet). Confirm on site before setting out.
7. Corridor windows facing the courtyard provide daylight and cross-ventilation. Louvred fanlights over guest-room doors.
8. All external doors and ground-floor windows to be burglar-proofed. Exit doors open outward.
9. Rear yard kept clear. Septic tank, soakaway and water supply positions to be agreed with the plumbing engineer.
10. Generator room: louvred double door, exhaust vented to open air, away from guest rooms.
11. Read with structural, electrical and plumbing drawings. To be checked by a registered architect/engineer before construction.

REVISIONS

REV	DATE	DESCRIPTION
P1	05/11/2026	Preliminary issue for client review
P2	05/11/2026	Lounge enlarged (no corridor); corridor end doors removed; rear yard cleared

PROJECT

PROPOSED TOCHI HOTEL

Single-storey, 13 en-suite guest rooms · lounge/bar · kitchen

DRAWING TITLE

GROUND FLOOR PLAN & SITE LAYOUT

CLIENT: _____	LOCATION: _____
SCALE: **1:100 & 1:150 @ A1**	DATE: **05 NOVEMBER 2026**
DRAWING NO.: **TH-A-101**	REVISION: **P2**
SHEET: **1 OF 1**	STATUS: **PRELIMINARY**
CHECKED BY: _____	APPROVED BY: _____

DRAWN BY

Engr. Chinemenum Paul Ogbonda

Signature: _____

NOT FOR CONSTRUCTION — FOR CLIENT REVIEW